
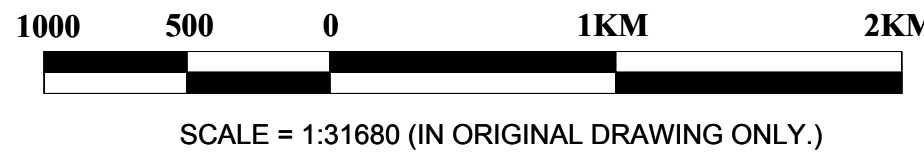


DRAFT DEVELOPMENT PLAN - 2031 A.D.
(UNDER SECTION 5(4) OF PUNJAB ACT NO. 41 OF 1963)

100	RESIDENTIAL	
	RESIDENTIAL SECTOR ON NEIGHBOURHOOD PATTERN	
200	COMMERCIAL	
210	RETAIL TRADE,	
220	WHOLE SALE TRADE	
230	WARE-HOUSING AND STORAGE.	
240	OFFICE AND BANKS INCLUDING GOVT. OFFICES.	
250	RESTAURANTS, HOTELS AND TRANSIT BOARDING HOUSES	
	INCLUDING PUBLIC ASSISTANCE INSTITUTIONS PROVIDING	
	RESIDENTIAL ACCOMMODATION LIKE DIHARAMSHALA, TOURIST HOUSES ETC.	
260	CINEMA, AND OTHER PLACES OF PUBLIC	
	ASSEMBLY ON A COMMERCIAL BASIS,	
270	PROFESSIONAL ESTABLISHMENTS	
300	INDUSTRIAL	
310	SERVICE INDUSTRY.	
320	LIGHT INDUSTRY.	
330	EXTENSIVE INDUSTRY.	
340	HEAVY INDUSTRY	
400	TRANSPORT & COMMUNICATION	
410	RAILWAY YARDS,RAILWAY STATIONS AND SIDING ROADS.	
420	ROADS,ROAD TRANSPORT DEPOTS AND PARKING- AREAS.	
450	TELEGRAPH OFFICES AND TELEPHONE EXCHANGES ETC.	
460	BROAD CASTING STATION	
470	TELEVISION STATION	
500	PUBLIC UTILITIES	
510	WATER SUPPLY INSTALLATIONS INCLUDING TREATMENT PLANTS.	
520	DRAINAGE AND SANITARY INSTALLATIONS INCLUDING DISPOSAL WORKS.	
530	ELECTRIC POWER PLANTS, SUB STATIONS ETC.	
540	GAS INSTALLATION AND GAS WORKS	
550	SOLID WASTE	
600	PUBLIC & SEMI PUBLIC	
610	GOVT. ADMINISTRATIVE,CENTRE, SECRETARIAT, DISTRICT OFFICES	
	LAW COURTS, JAIL & POLICE STATION.	
	GOVERNORS AND RESIDENT'S, RESIDENCE.	
620	EDUCATIONAL,CULTURAL AND RELIGIOUS INSTITUTIONS.	
630	MEDICAL AND HEALTH INSTITUTIONS.	
640	CULTURAL INSTITUTION LIKE THEATERS, OPERA HOUSES ETC.	
	OF A PREDOMINANTLY NON-COMMERCIAL NATURE.	
700	OPEN SPACES	
710	SPORTS GROUNDS,STADIUM AND PLAY GROUNDS	
720	PARKS.	
730	GREEN BELTS, GARDEN AND OTHER RECREATIONAL USES.	
740	CEMETERIES, CREMATORIS ETC	
750	FUEL FILLING STATIONS AND BUS QUEUE SHELTERS.	
800	AGRICULTURAL LAND	
810	MARKET GARDEN	
820	ORCHARDS AND NURSERIES	
830	LAND UNDER STAPLE CROPS.	
840	GRAZING AND LAND PASTURES.	
850	FOREST LAND	
860	MARSHY LAND	
870	BAREN LAND	
880	LAND UNDER WATER.	
890	DAIRY FARM.	
	EXISTING FEATURES	
	SECTOR NO.	(5)
	EXISTING BUILT UP AREA	
	VILLAGE ABADI - DEH.	
	ROAD & KATCHA RASTA.	
	RING BUND/ DRAIN	
	DISTRIBUTARY/ MINOR	
	CONTROLLED AREA BOUNDRY.	
	M.C. LIMIT BOUNDRY.	
	RAILWAY LINE	
	PROPOSED RESIDENTIAL DENSITY/HECT.	
		250

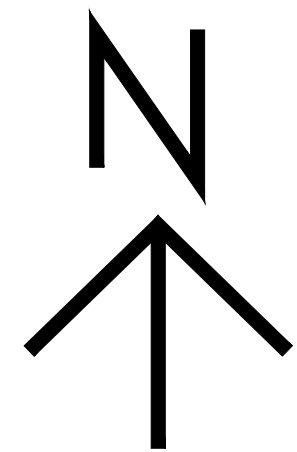

DRG. NO. D.T.P. (JH) 368 / 10 DATED 05 - 07 - 2010
28 - 02 - 2011

DRAWN BY SD /- (SATISH KUMAR)
JD.

CHECKED BY SD /- (MUNI RAM)
SD.


PLANING ASSTT.	VACANT
----------------	--------

ASSTT. TOWN PLANNER SD /- (J. P. KHASA)



DISTT. TOWN PLANNER SD /- (ANIL DABAS)

SENIOR TOWN PLANNER, ROHTAK	SD /- (YUSUF MOHD. MANSURI)	CHIEF CO-ORDINATOR PLANNER N.C.R HARYANA, PANCHKULA
--------------------------------	--------------------------------	--

DEPTT. OF TOWN & COUNTRY PLANNING HARYANA, CHANDIGARH

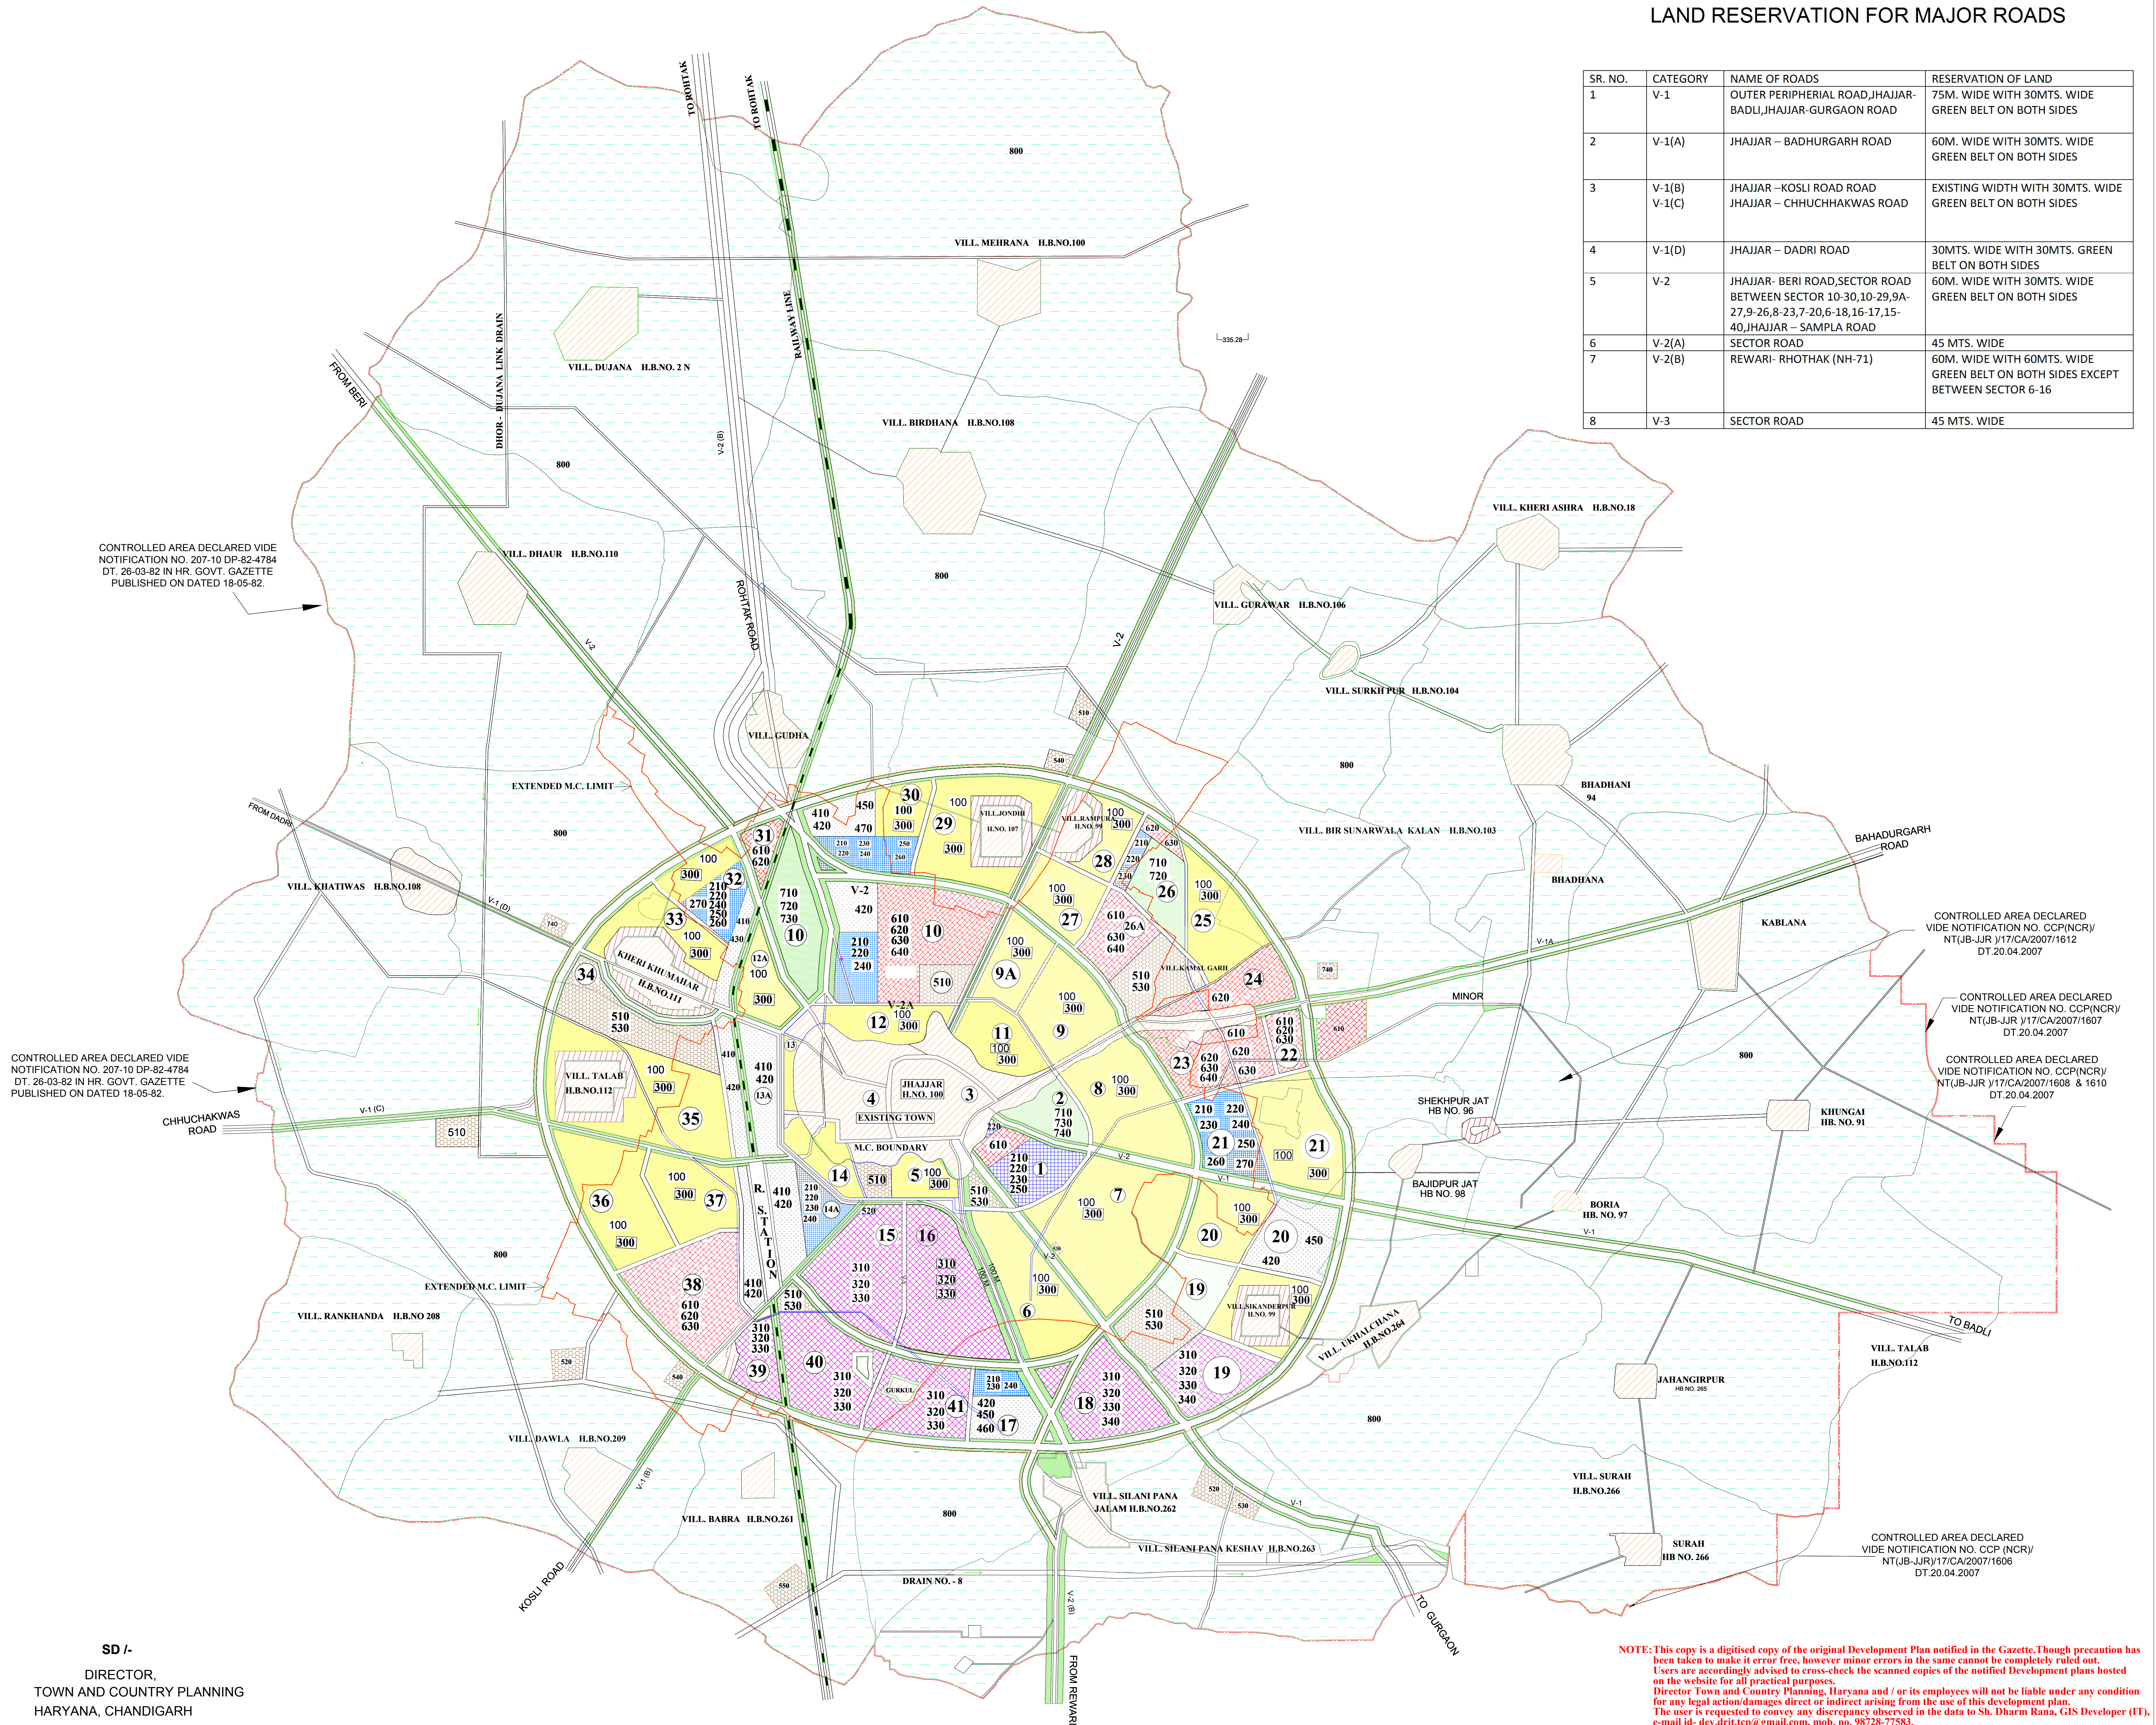

Kheri_Asra

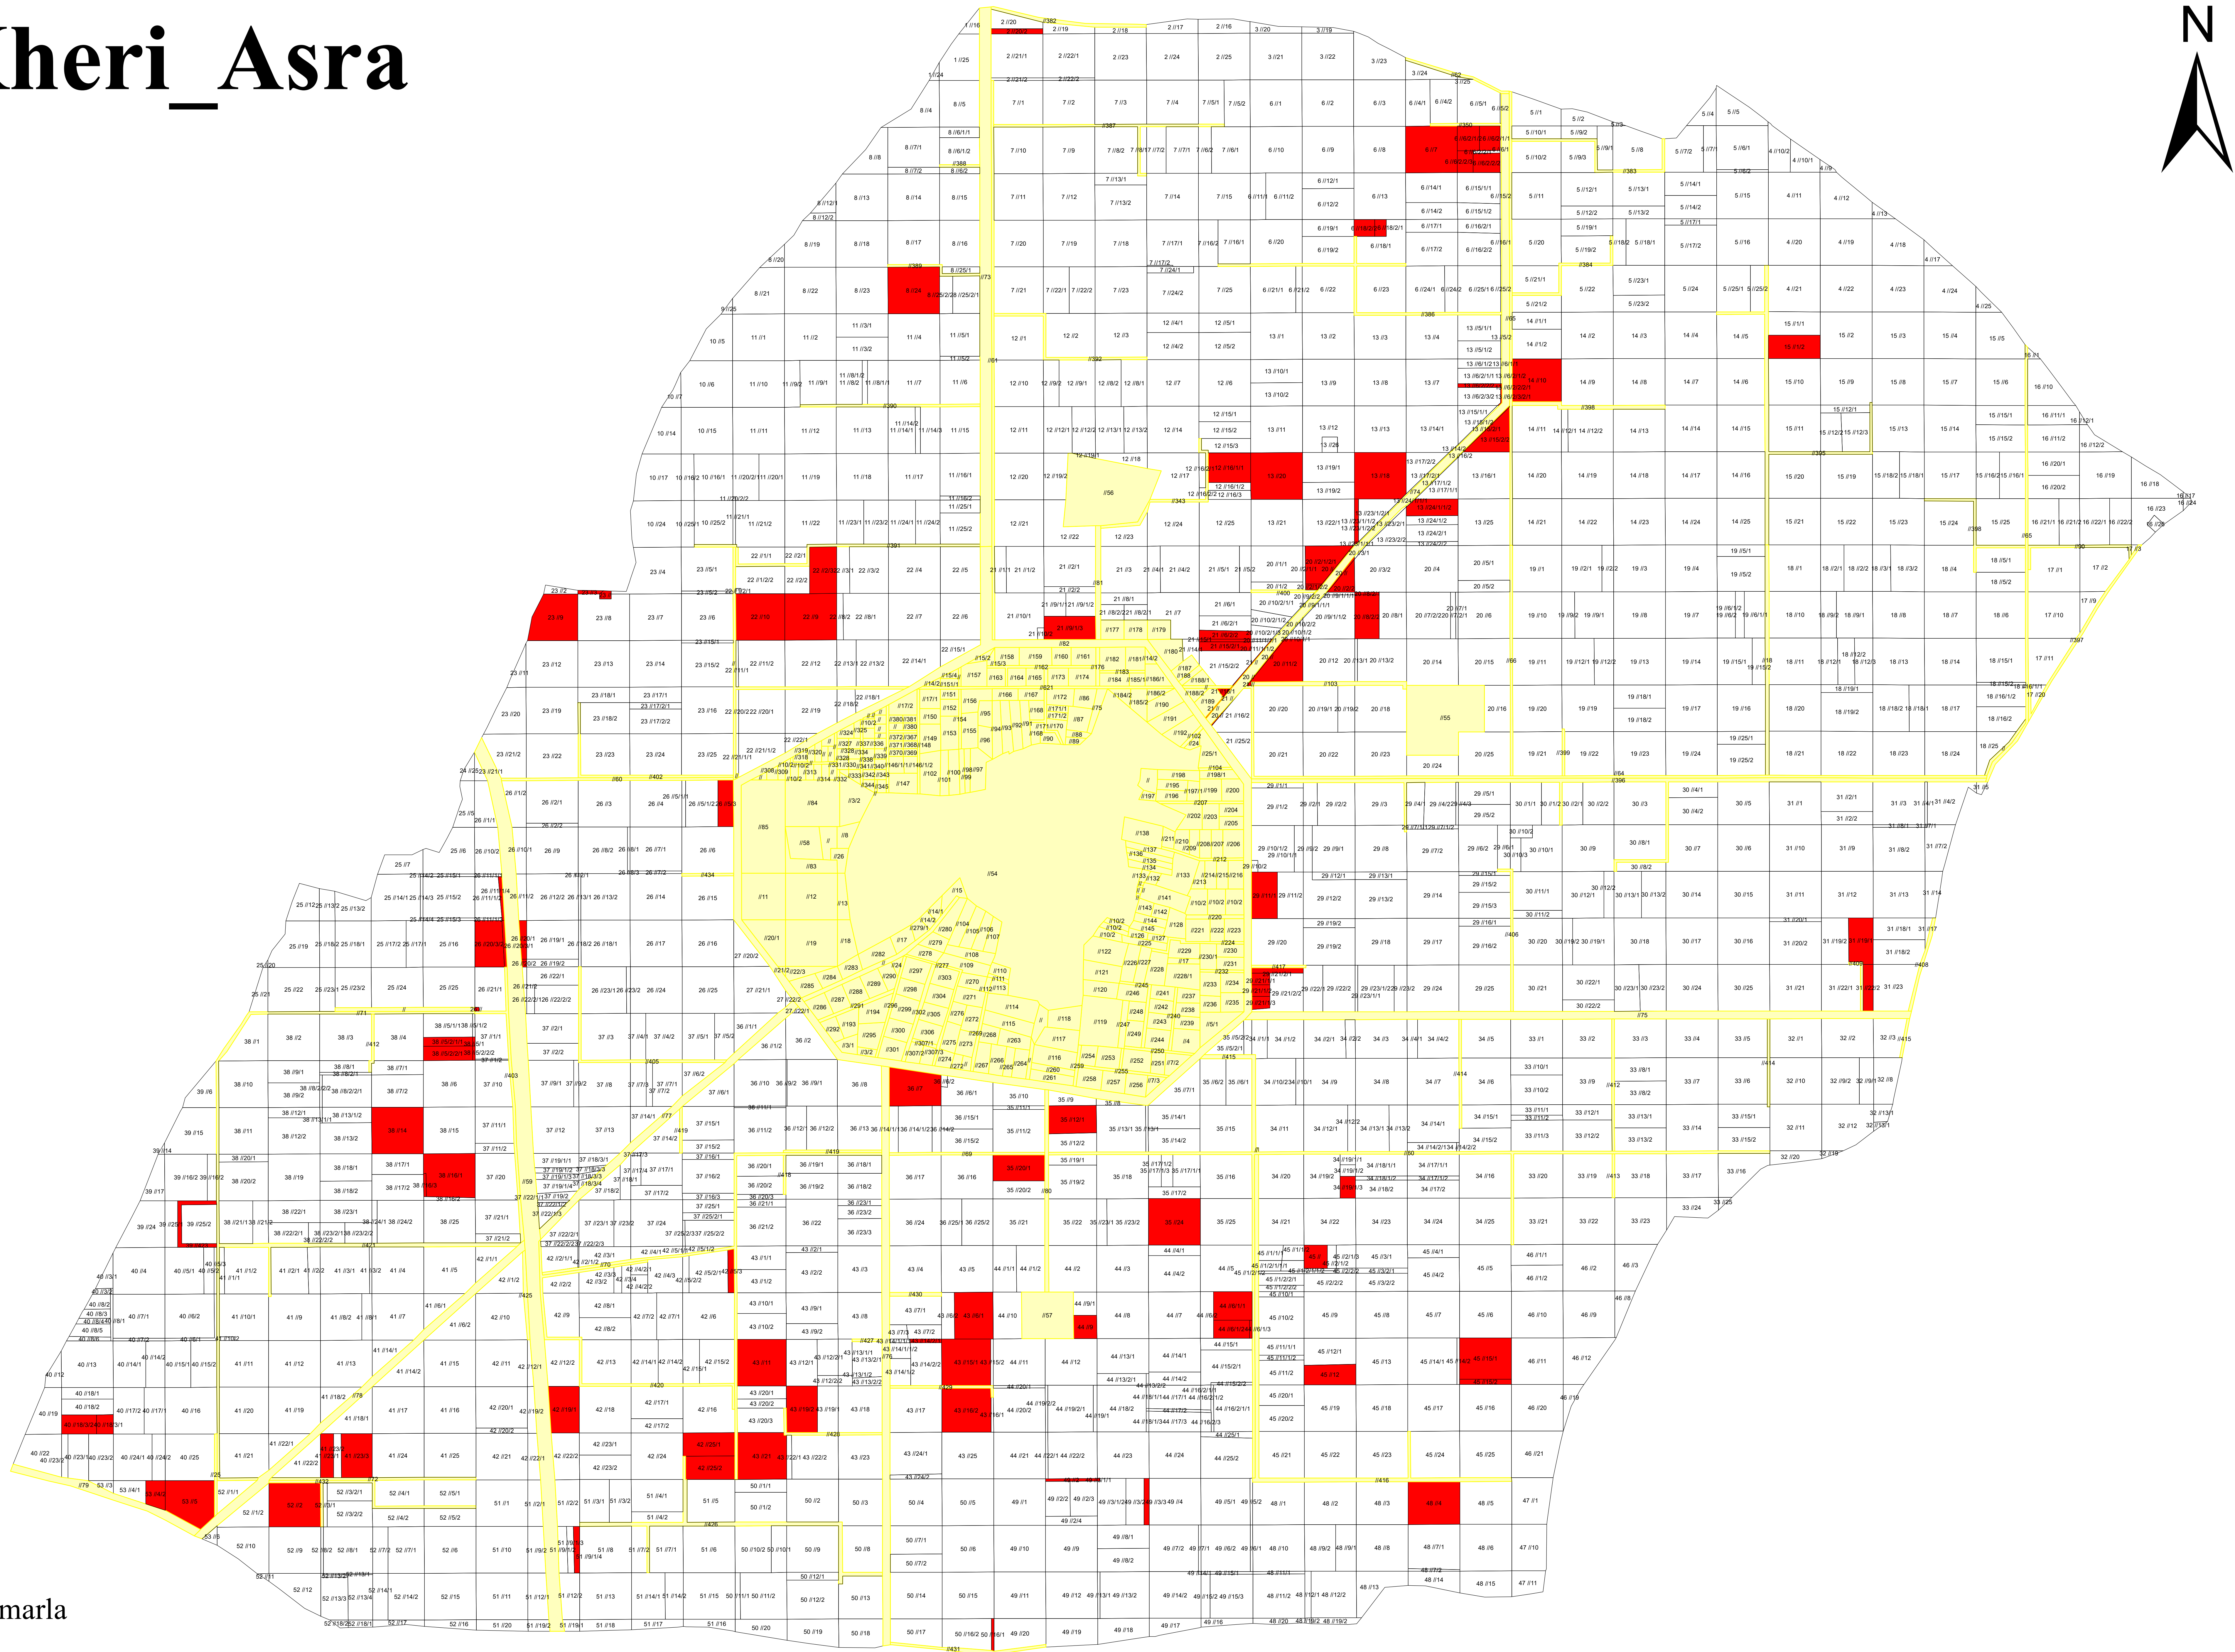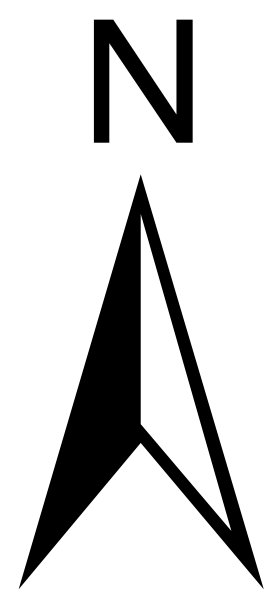


Legend Kheri_Asra Remarks

- ☐ Area matched
- ☐ Area matched in 1 marla
- ☐ Area not matched
- ☐ Bada_No
- ☐ Tatime required

0 0.1 0.2 0.4 0.6 0.8 Kms

PLOT NO :- 63 & 64

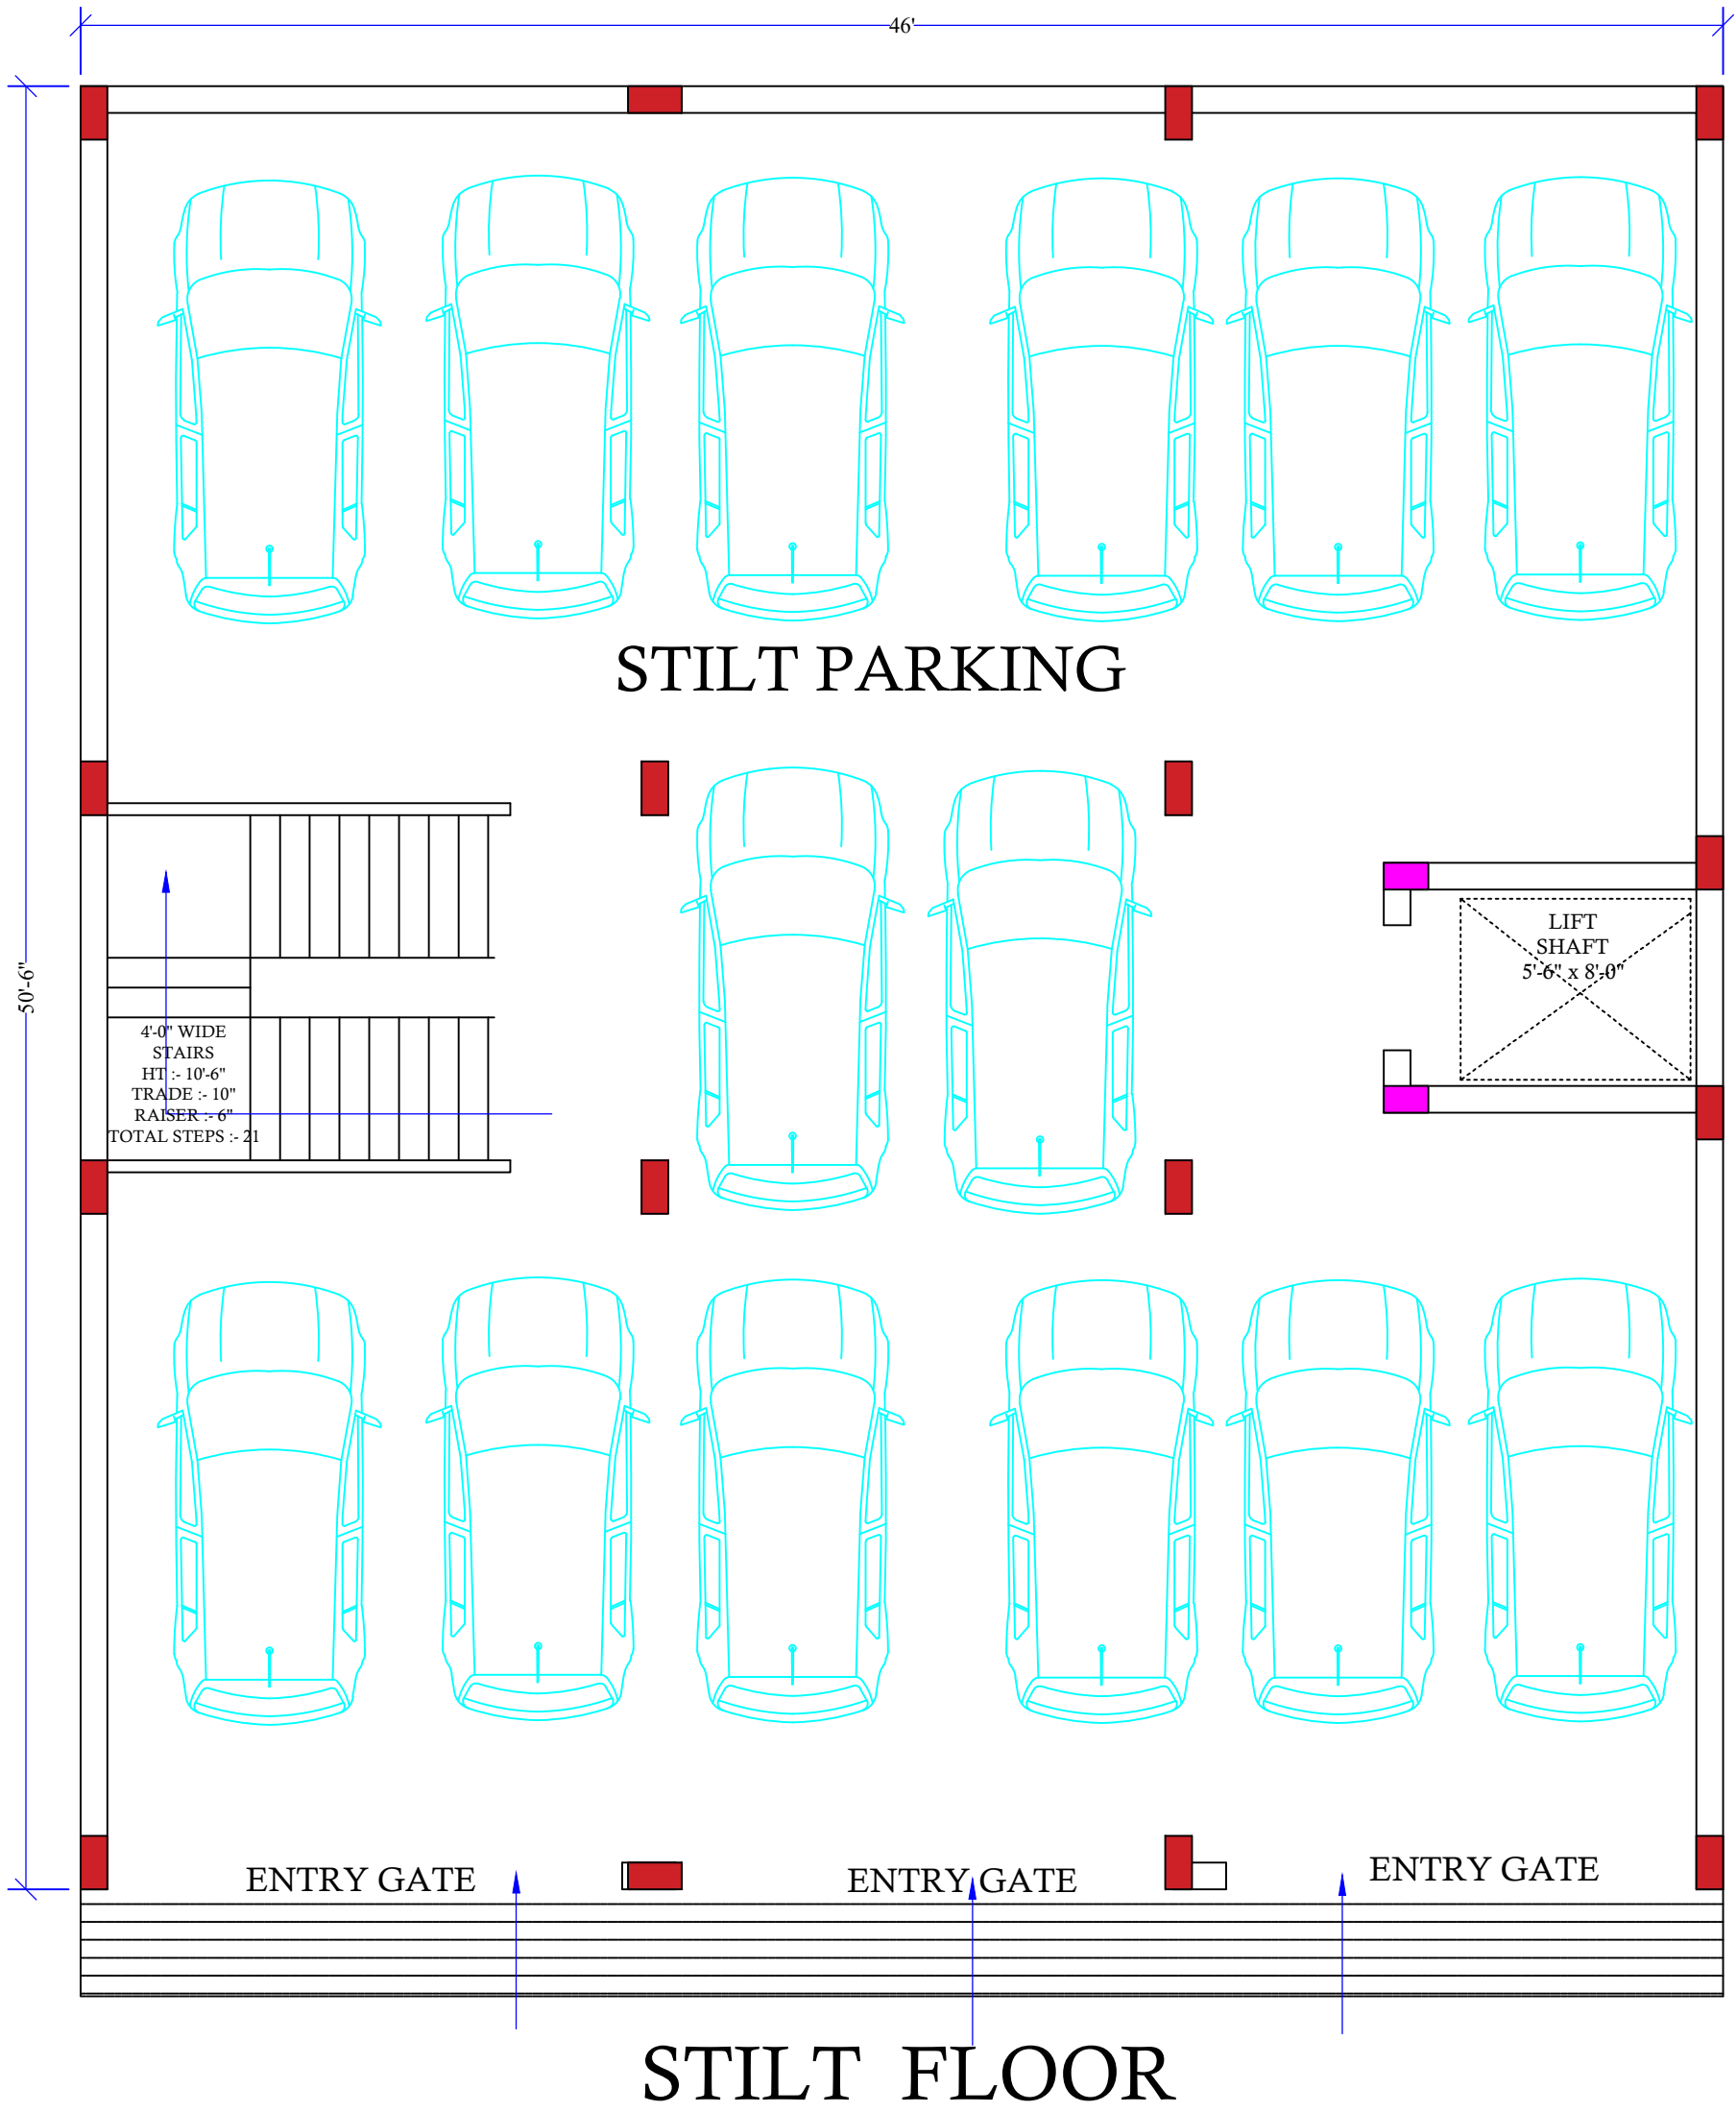



THE VISION ARCHITECTS & CONSULTANT

ARCHITECTURE | INTERIOR DESIGN | EXTERIOR DESIGN | STRUCTURAL CONSULTANCY | VALUATION

Office: Near Civil Hospital, Farrukh Nagar, Gurugram, HR.122506

7206248656

AR. YASH GARG
(B.Arch, M.Arch)



Architectural Design



Interior Design



Exterior Design




Structural Consultancy



Valuation Services

PLOT NO :- 63 & 64

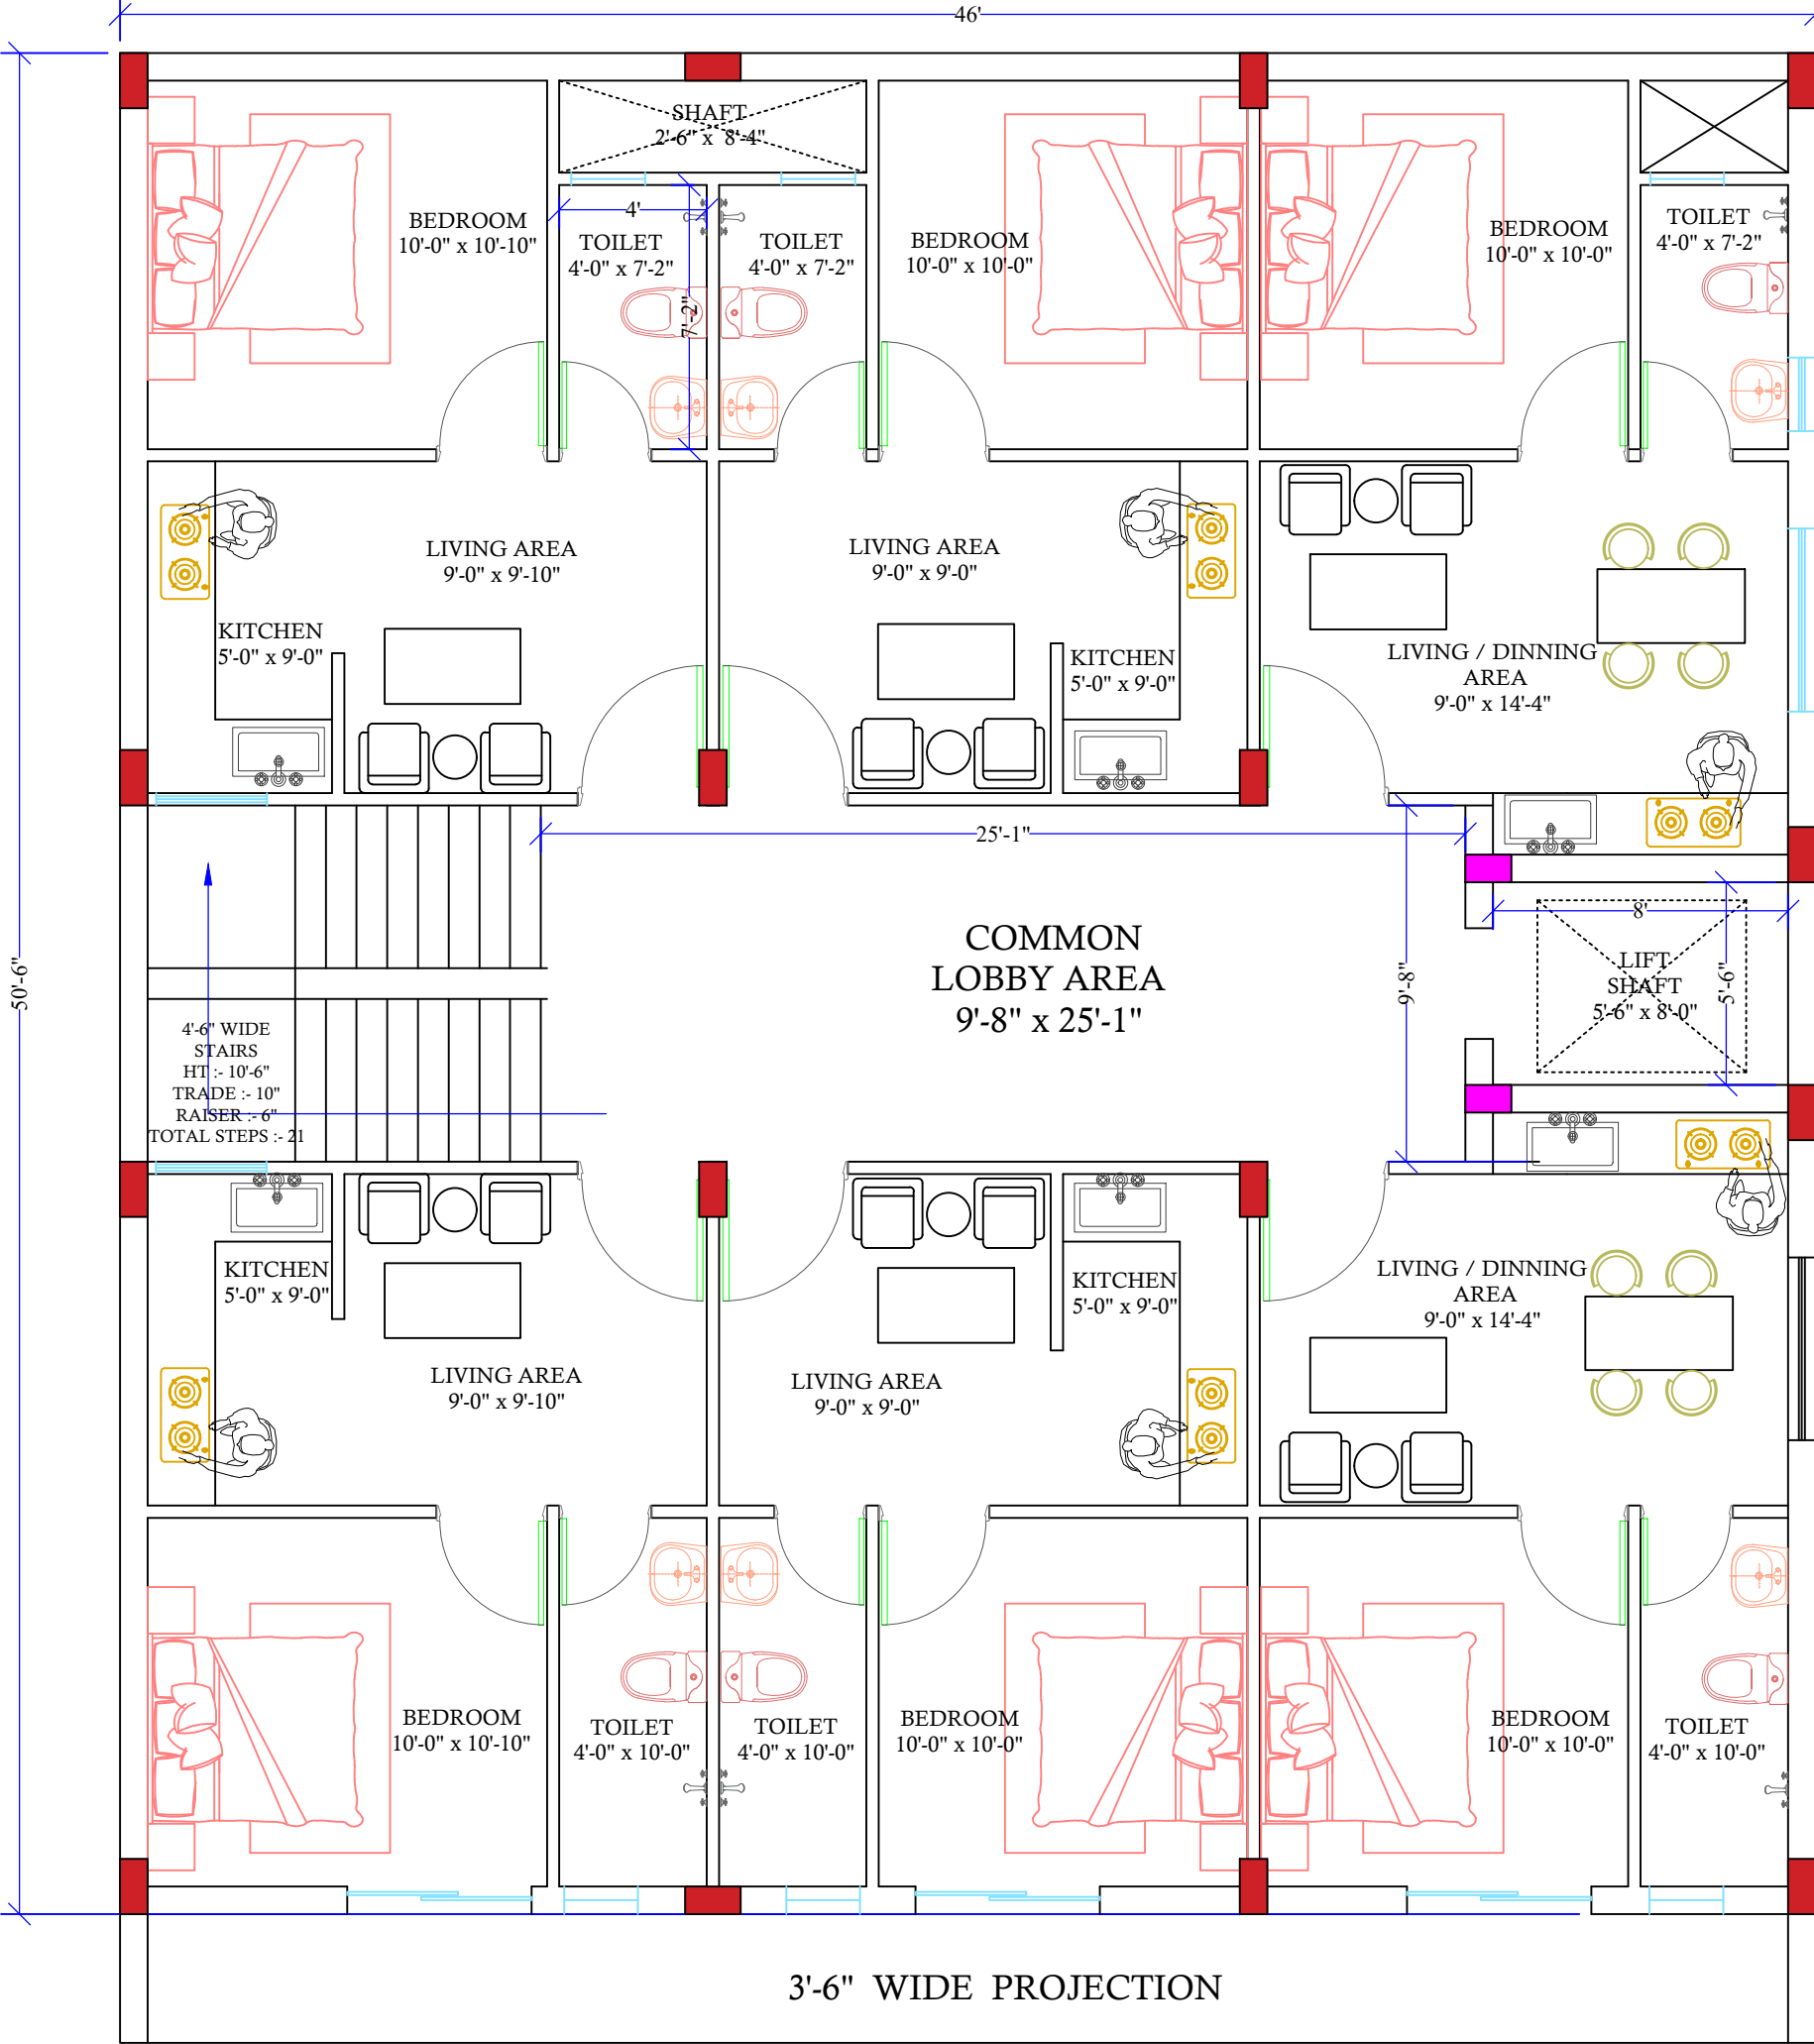

TYPICAL FLOOR



THE VISION ARCHITECTS & CONSULTANT
ARCHITECTURE | INTERIOR DESIGN | EXTERIOR DESIGN | STRUCTURAL CONSULTANCY | VALUATION

Office: Near Civil Hospital, Farrukh Nagar, Gurugram, HR.122506

7206248656

AR. YASH GARG
(B.ARCH, M.ARCH)



Architectural Design Interior Design Exterior Design Structural Consultancy Valuation Services

"SENIOR LIVING CITIZEN FOUNDATION."

